
PLOT 83 / NEW CAIRO

B1 / BASEMENT -3.20 m


17.00 m E-W x 25.00 m N-S / CAD SET

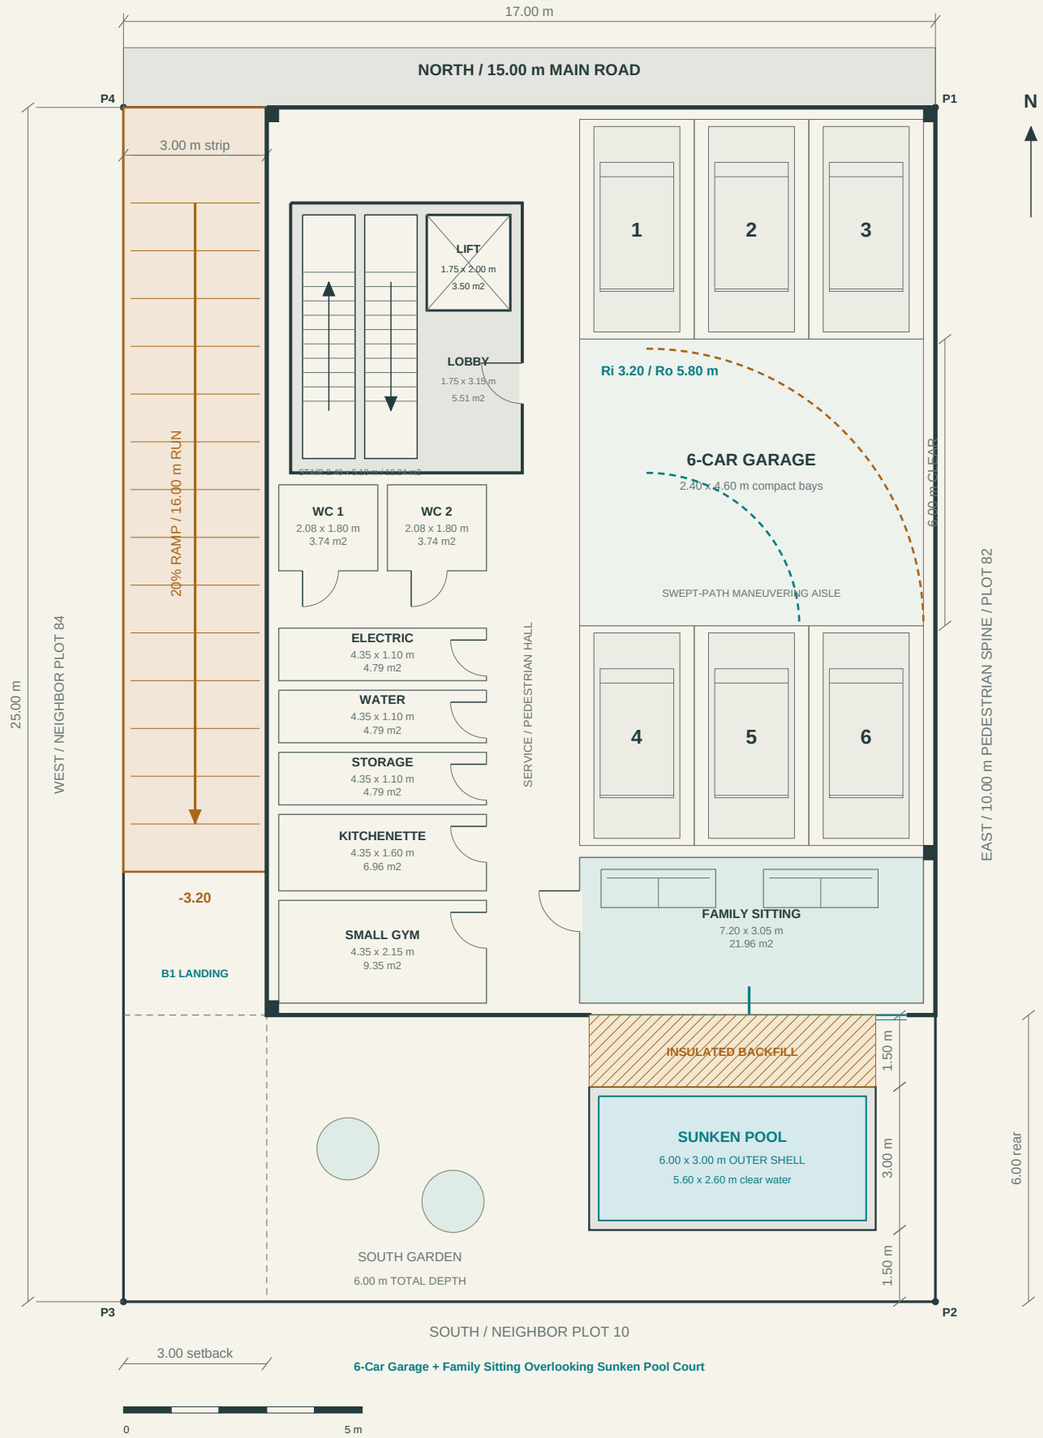

PLOT 83 / NEW CAIRO

00 / GROUND +0.45 m


17.00 m E-W x 25.00 m N-S / CAD SET

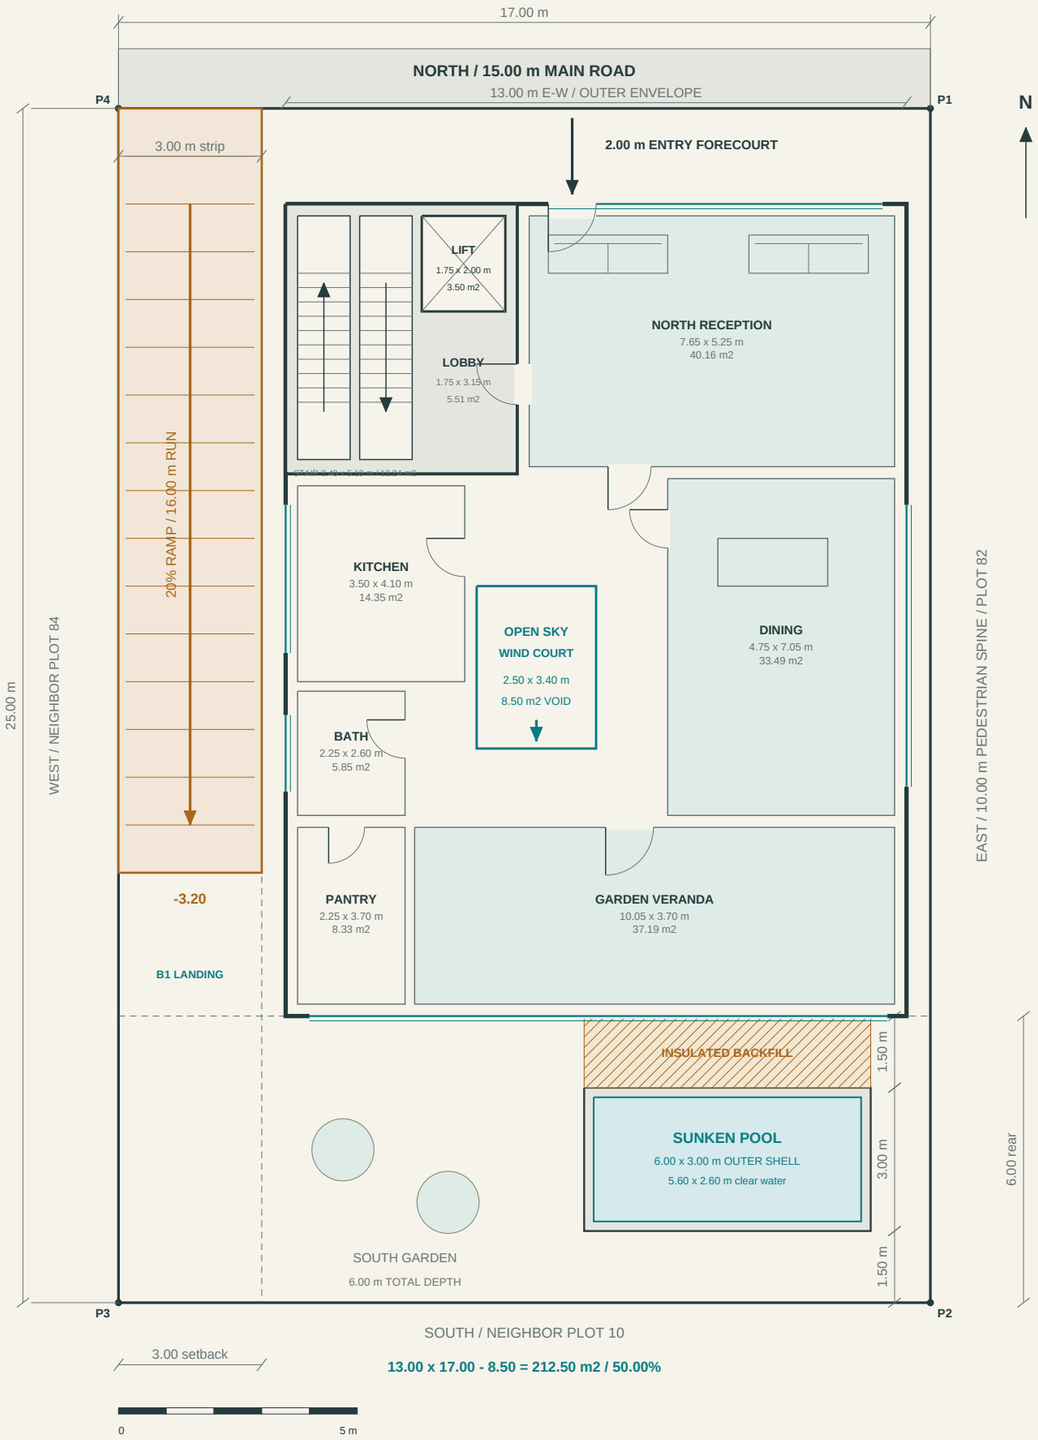

PLOT 83 / NEW CAIRO

01-03 / TYPICAL +3.75 / +7.05 / +10.35 m


17.00 m E-W x 25.00 m N-S / CAD SET

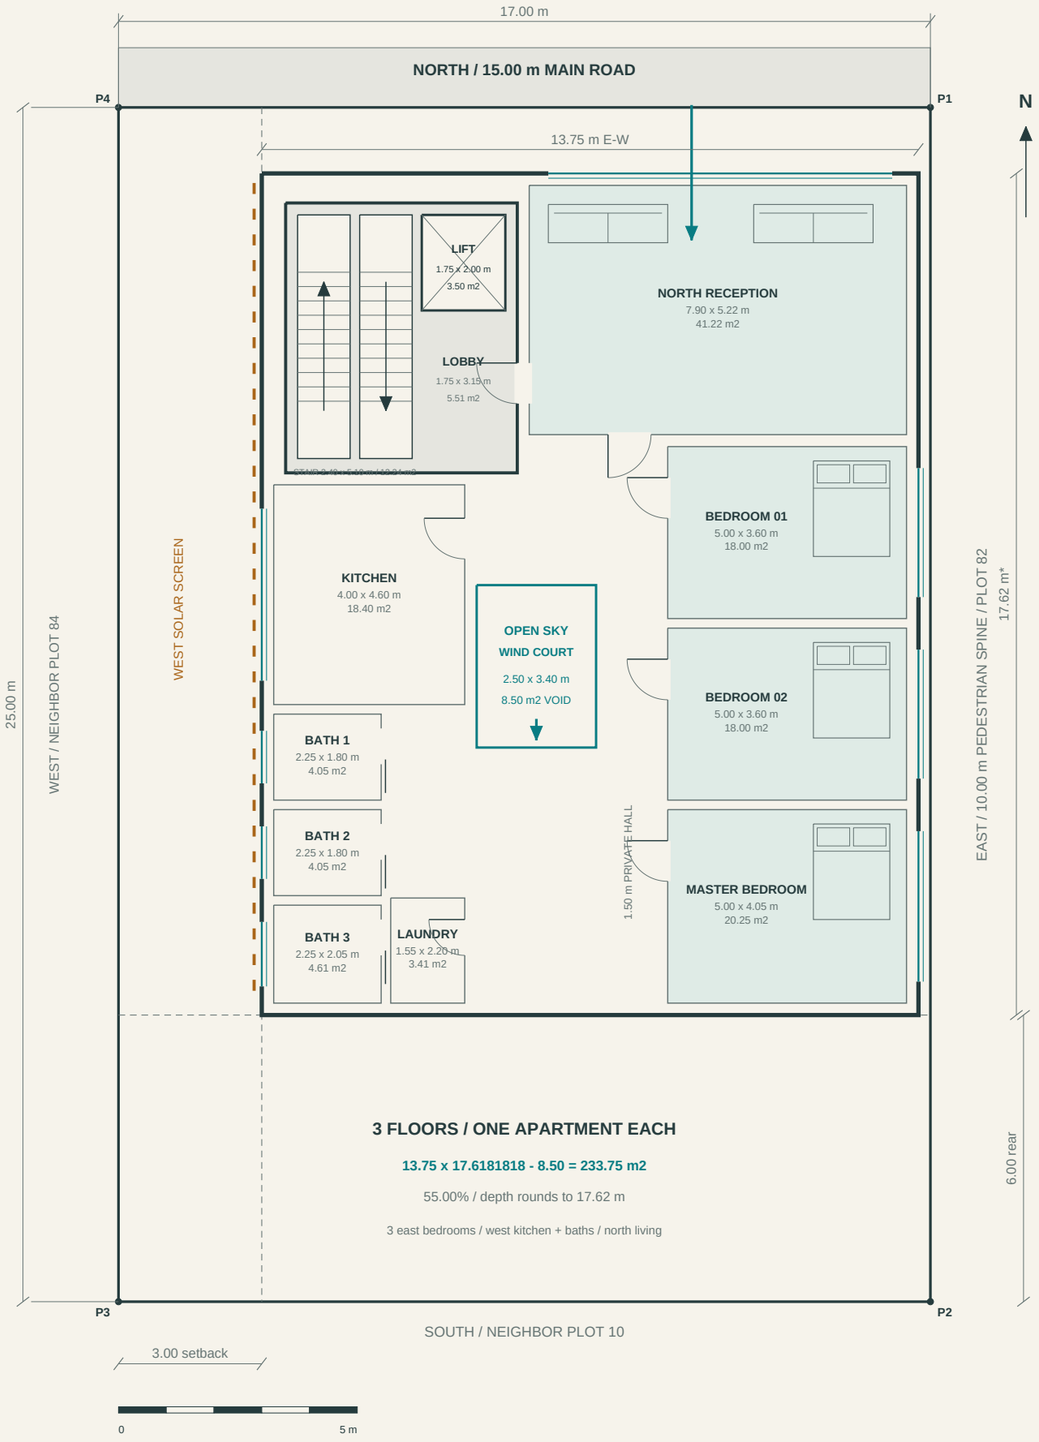

PLOT 83 / NEW CAIRO

R / ROOF +13.65 m


17.00 m E-W x 25.00 m N-S / CAD SET

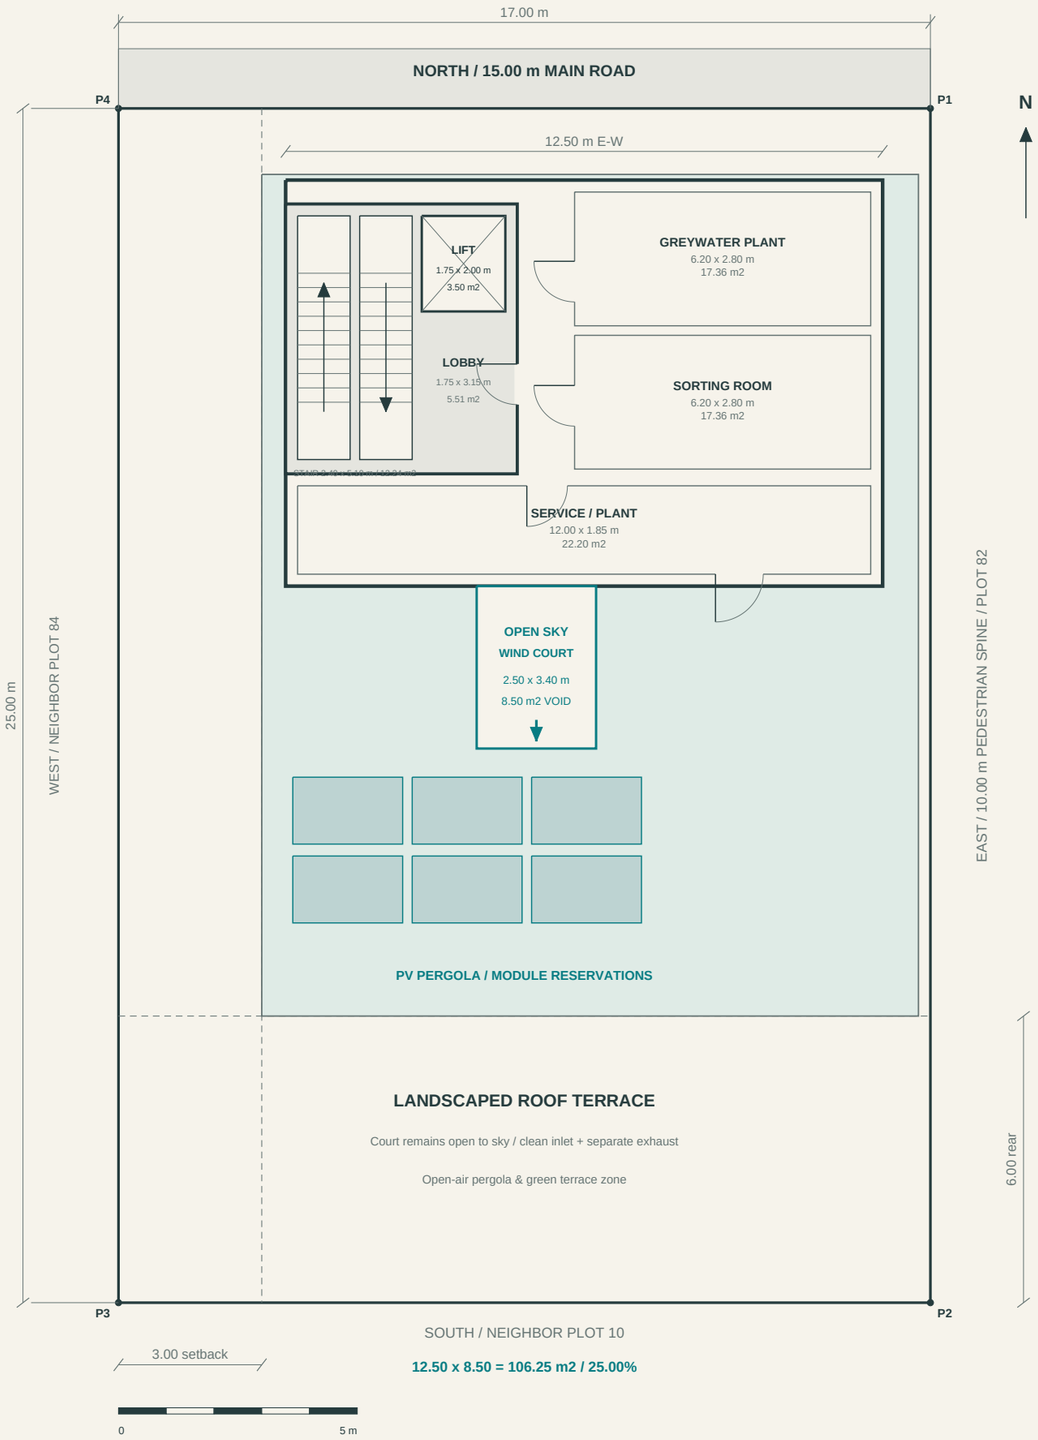

PLOT 83 / NEW CAIRO

A-A / NORTH-SOUTH ENVIRONMENTAL SECTION

17.00 m E-W x 25.00 m N-S / CAD SET

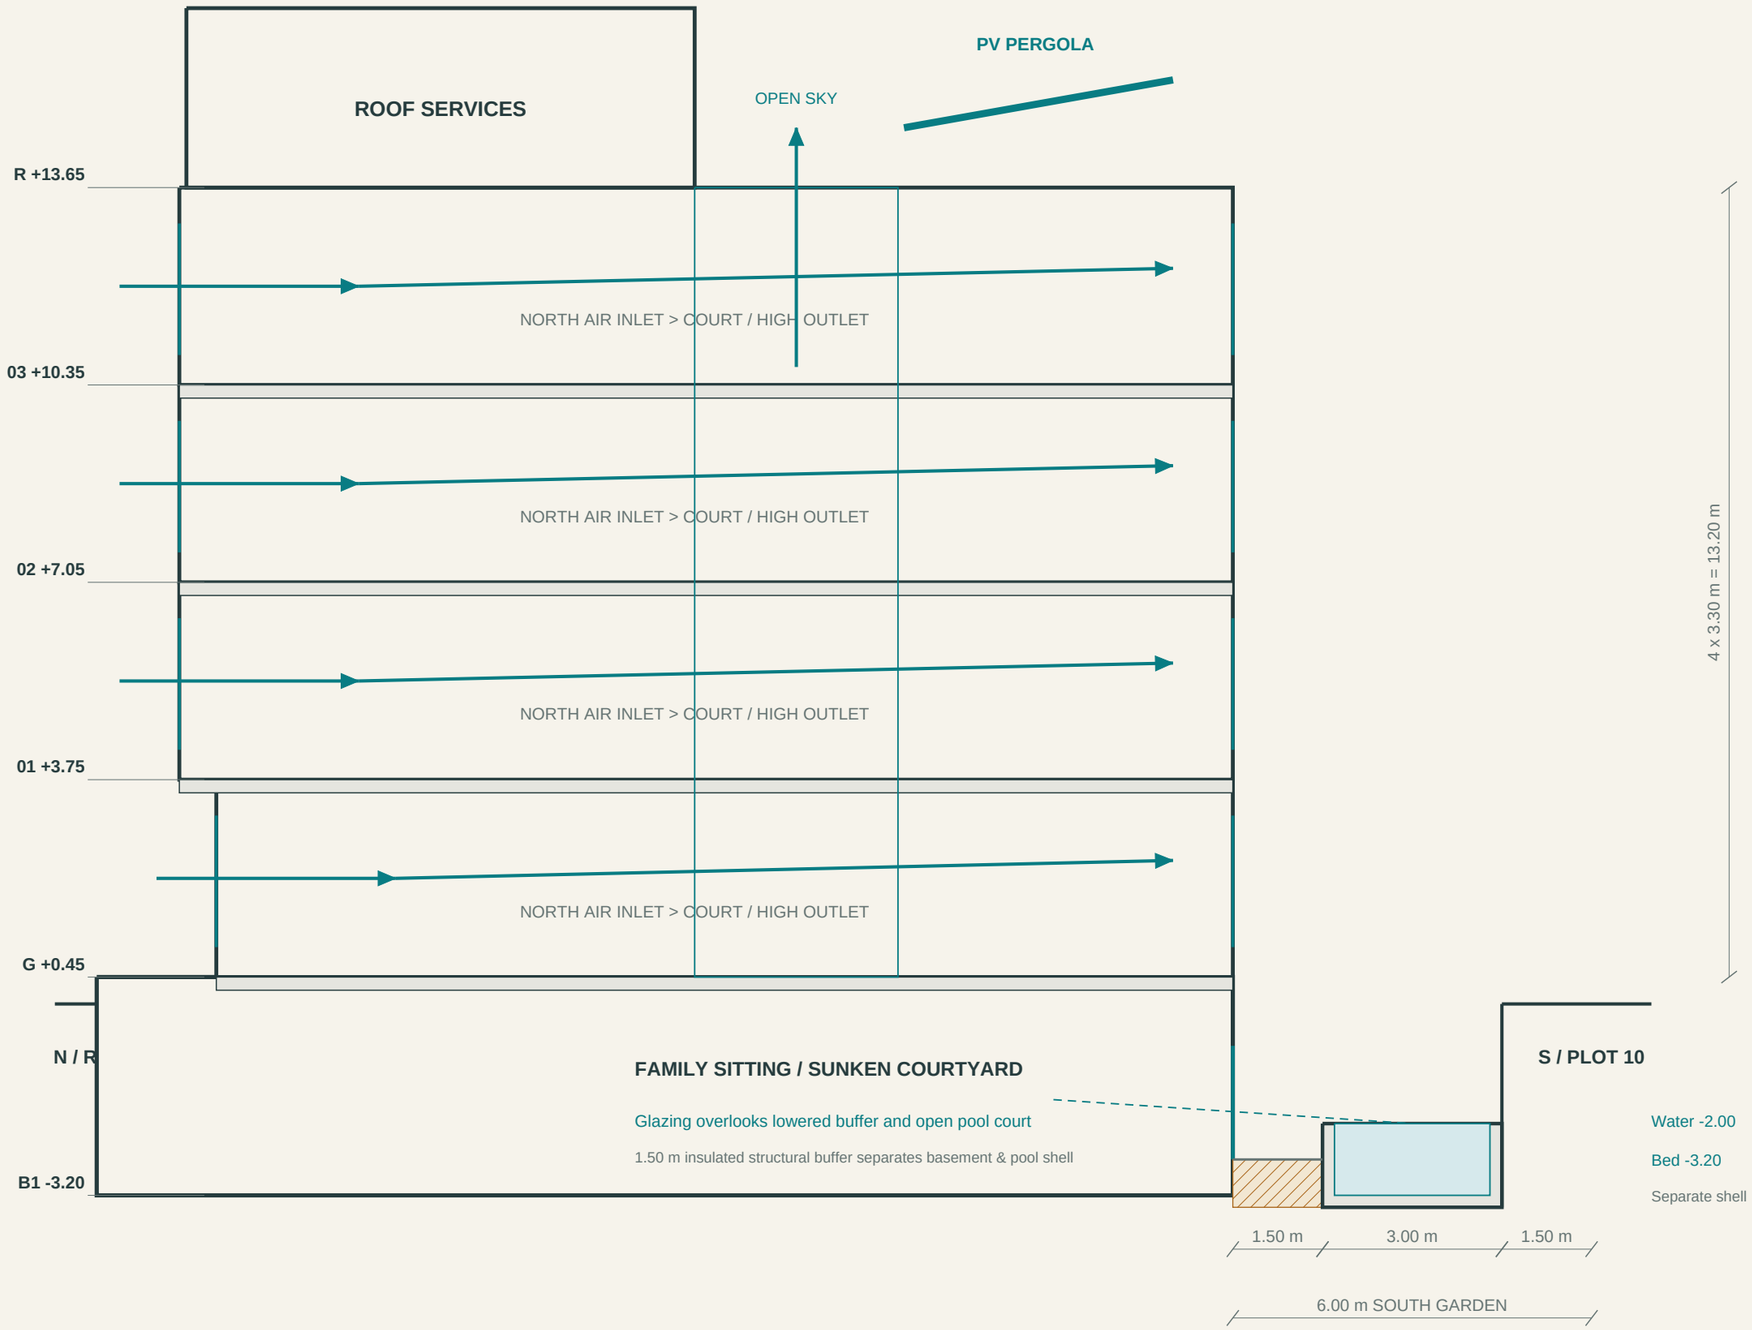


SECTION A-A / North-South environmental section through wind court & sunken pool

PLOT 83 / NEW CAIRO

P / PASSIVE SOLAR + WIND STUDY

17.00 m E-W x 25.00 m N-S / CAD SET

N / NW BREEZE

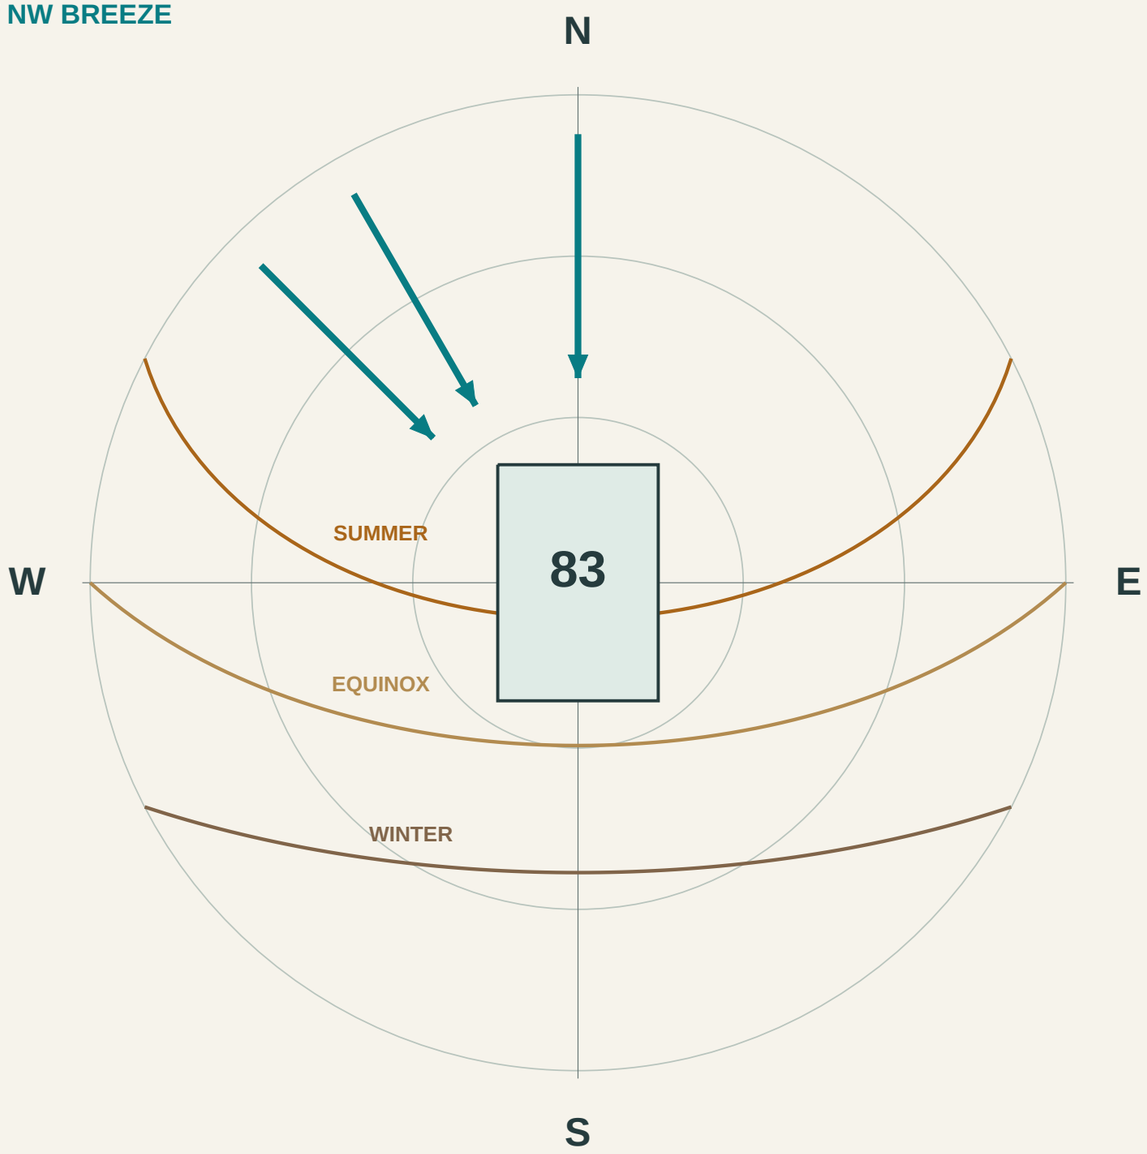


New Cairo latitude assumption: 30.03 N / true north

Jun: noon 83.41 deg **Mar/Sep: noon 59.97 deg** **Dec: noon 36.53 deg**


Prevailing N/NW summer breeze + calculated solar paths (30.03 deg N).

West mashrabiya + east morning light + north cross-ventilation.

A / WRAPPED LIFT

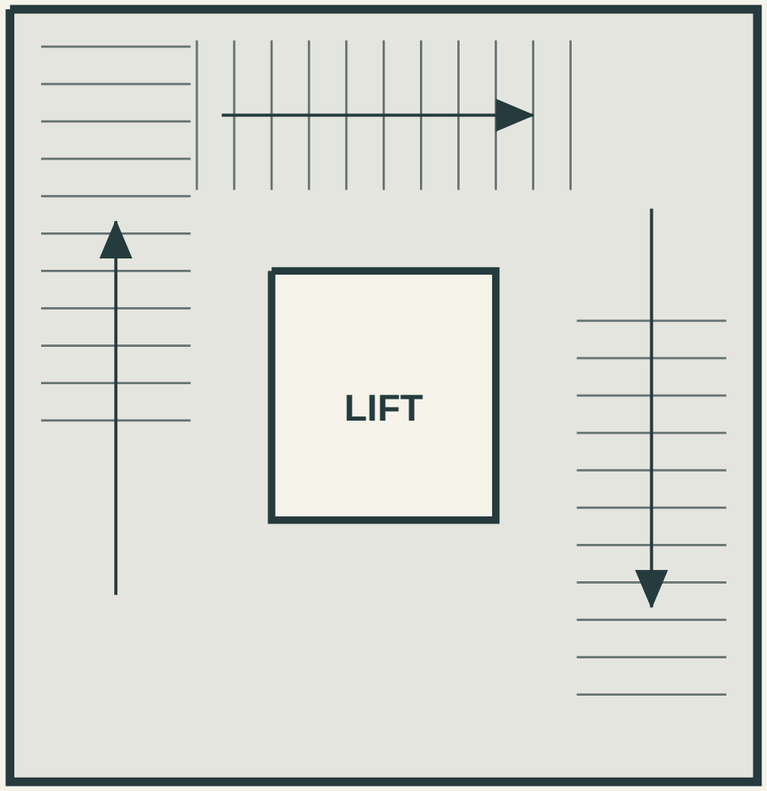

B / ADJACENT U-STAIR

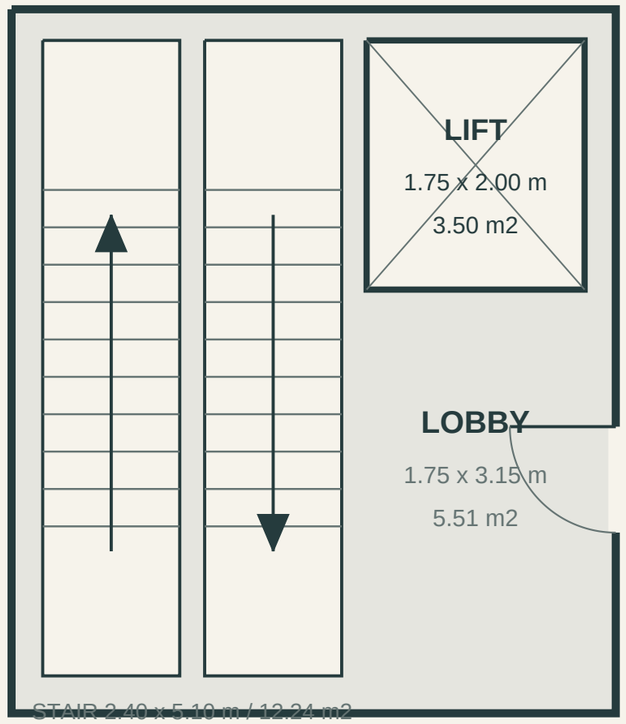

A core reservation: 37.20 m2

Multi-direction landings / more wall returns

B core reservation: 27.40 m2

SELECTED / aligned shear-wall layout

Net-to-gross efficiency: A 84.09% / B 88.28% (+4.19% floor plate gain)


COMPACT SIDE-BY-SIDE CORE SAVES 9.80 m2 PER FLOOR PLATE.

Identical gross floor plate; aligned 2-flight U-stair + 8-person lift.

PLOT 83 / NEW CAIRO

S0 / SOURCE SURVEY ORIENTATION

17.00 m E-W x 25.00 m N-S / CAD SET

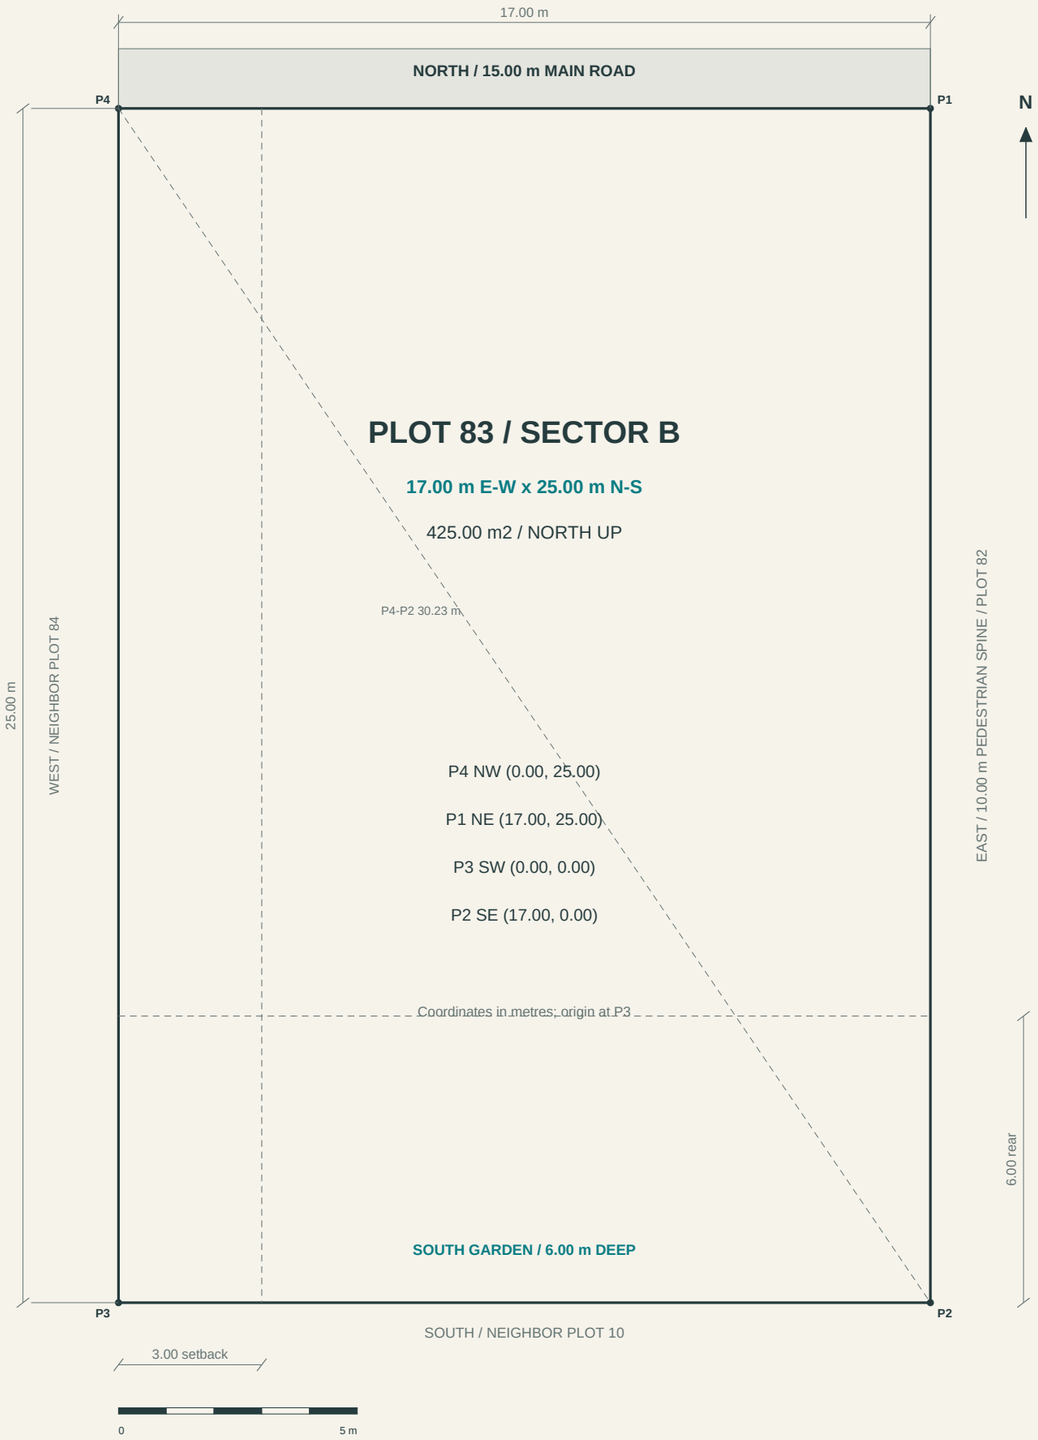

AREA / OUTER FOOTPRINT LESS OPEN COURT

LAND	1 x 425.00 m2	100% of land
GROUND	1 x 212.50 m2	50% of land
TYPICAL	3 x 233.75 m2	55% of land
ROOF	1 x 106.25 m2	25% of land

TOTAL ABOVE GROUND: 1020.00 m2 / basement excluded

HOLD POINTS / DO NOT ISSUE FOR CONSTRUCTION

H01 / RAMP CONNECTION / SWEPT PATH

3.00 m west strip; 20% x 16.00 m nominal run. Transitions and garage link unresolved.

H02 / SUNKEN POOL / RETAINING

6 x 3 m outside shell; 1.50 m building buffer + 1.50 m south-fence clearance.

H03 / AREA MEASUREMENT

Ground221.00-8.50=212.50; typical242.25-8.50=233.75; roof106.25 m2.

H04 / CORE / STRUCTURE / SERVICES

Core B selected. Fire, egress, structure, lift and services remain schematic.